

*Phase
1*

OCCUPANCY OF HANIFA SULEMAN DAWOOD ONCOLOGY CENTRE

PHASE - 1

Basement:

- Laundry / Press Room
- Oxygen Plant
- Fumigation Office
- Store (Miscellaneous Articles)
- Store (EHR)

Ground Floor:

- Radiation Department
- AHU
- SECURITY ROOM

1st Floor:

- Oncology OPD
- Medical Onco (Chemotherapy Clinic)
- Diabetes Clinic
- Breast Clinic
- Cardiac Fitness Clinic
- General Anesthesia Clinic
- Onco – Uro Clinic, Head & Neck
- AHU

*Phase
1*

2nd Floor:

- Dressing Room
- Oncology Ward (Male 2,3 + Female 1)
- MIS Ward 1,2
- Pharmacy
- Dr. Room
- AHU
- Store

3rd Floor:

- Dr. Duty Room
- Vascular Ward (Male + Female)
- Neuro Physiology (EEG-EMG-NSC)
- EET
- Pleads Urology Ward
- MIS Male Ward 3,4
- AHU
- Robotic Surgery Ward (Male, Female)

4th Floor:

- Operation Theatre
- Auto Clave
- AHU

Please
1

5th Floor:

- Auditorium Hall
- Medical Education Deptt.
- Offices
- Jasmine Hall
- Female E.H.R Office
- AHU
- Store

6th Floor:

- Chiller Plant
- Diesel Generators
- Lift Room
- Faculties
- Common Stair case
- Emergency Stair Case
- 2 Lift

*Phase
II*

Phase – 2

Basement:

- Cold Storage (For Medicine)
- Store Miscellaneous
- Fire Pump/Pump Room
- Electrical Panel Room
- A.H.U

Ground Floor:

- CCTV Room + IT Room
- Miscellaneous CRS, Peads Cardiac, Peads Nephrology, Pleads Neuropath, Vascular
- Pump Area
- Gas Meter Room

1st Floor:

- Data Centre
- AHU Room
- Electrical Panel Room

2nd Floor:

- SCM Dept.
- Warehouse
- Electric Panel Room
- AHU

*Phase
II*

3rd Floor:

- Vascular Ward (Male + Female)
- HDU Ward
- MIS 3rd Ward
- Electric Room
- ID Office Female

4th Floor:

- Operation Theatre
- Electric Room
- Store Room
- AHU

5th Floor:


- Offices
- Electric Room
- Admission Room
- AHU


Rooftop:

- Oxygen Plant
- Medical Gases Plant Room
- Generator PAD
- Lift Room

Faculties:


- Common Stair case
- Emergency Stair Case
- 2 Lift

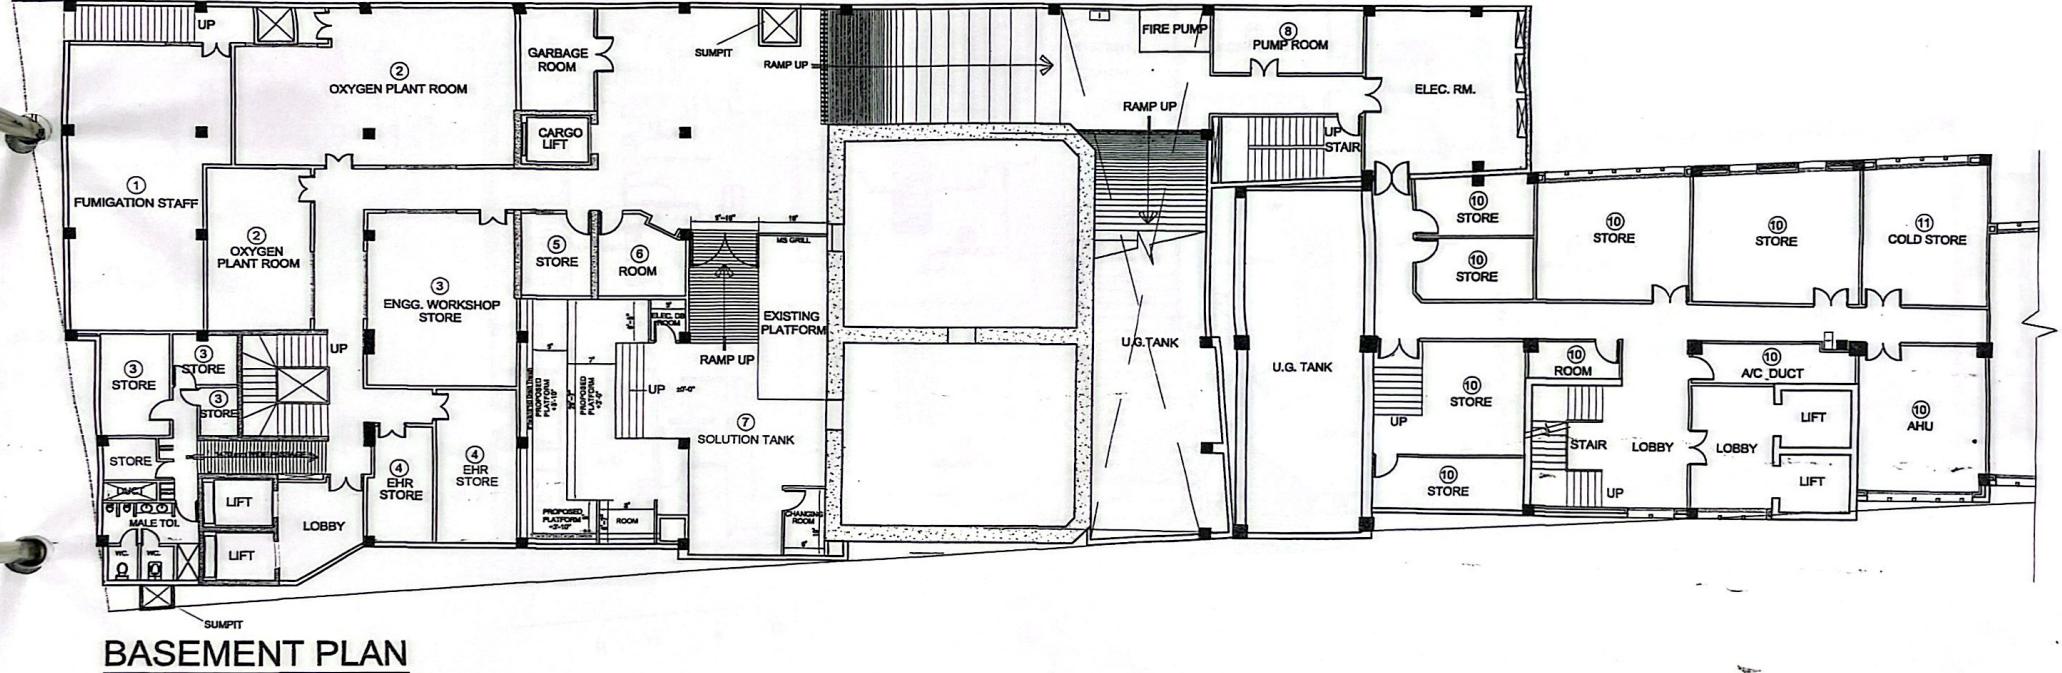

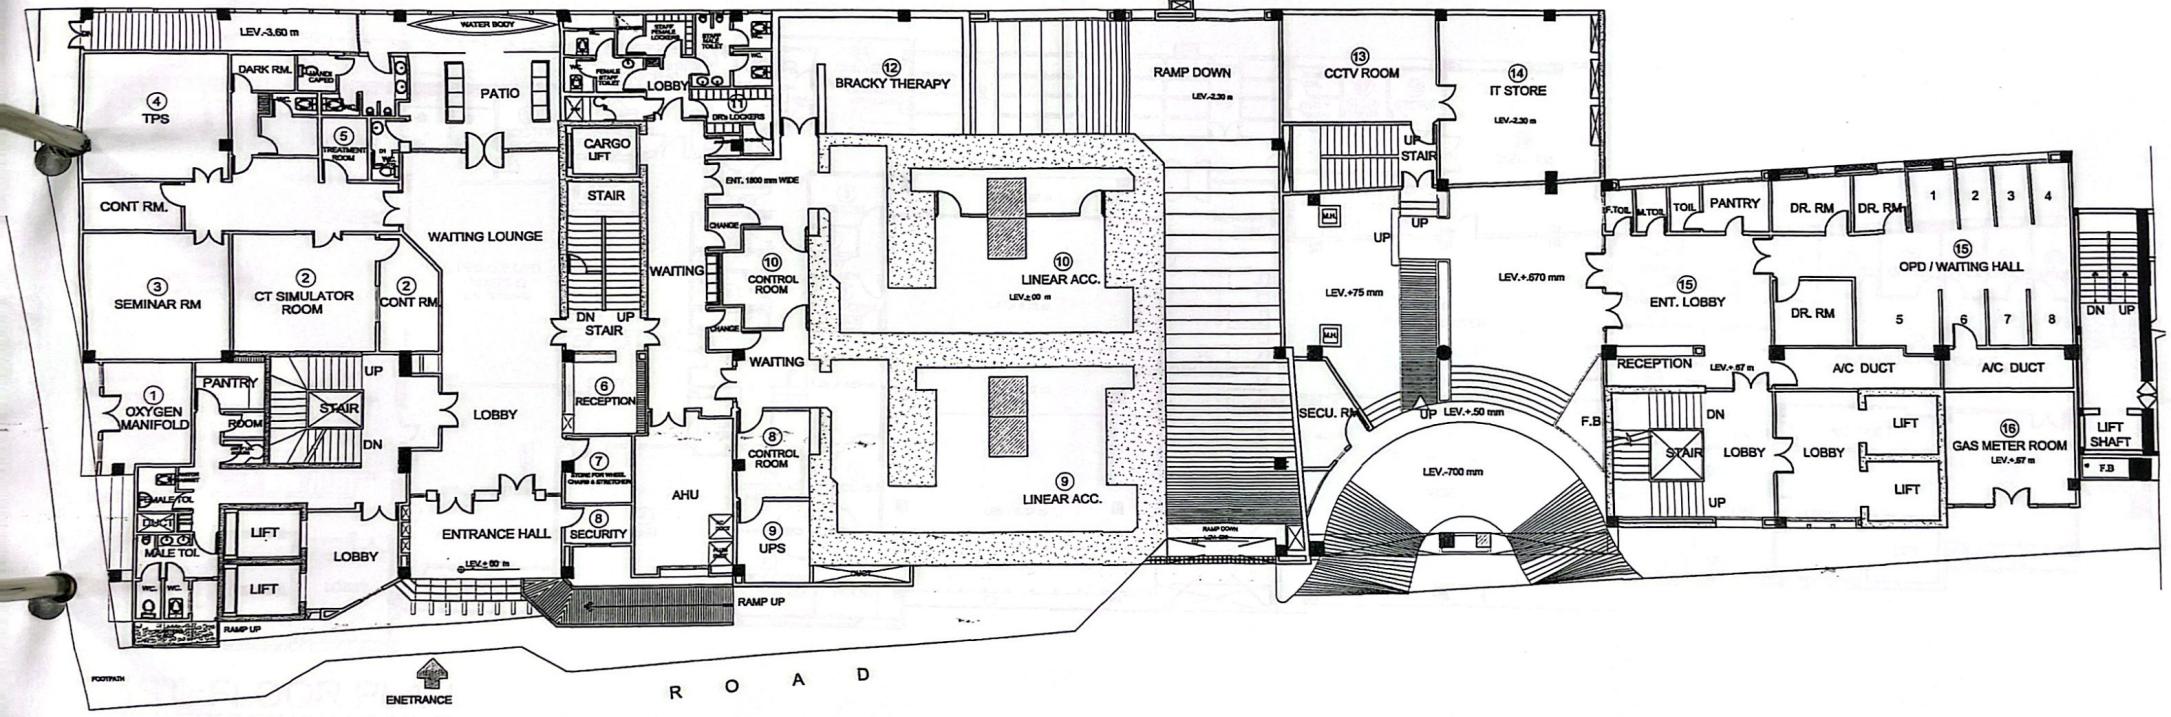


GR. FLOOR PLAN


1ST. FLOOR PLAN

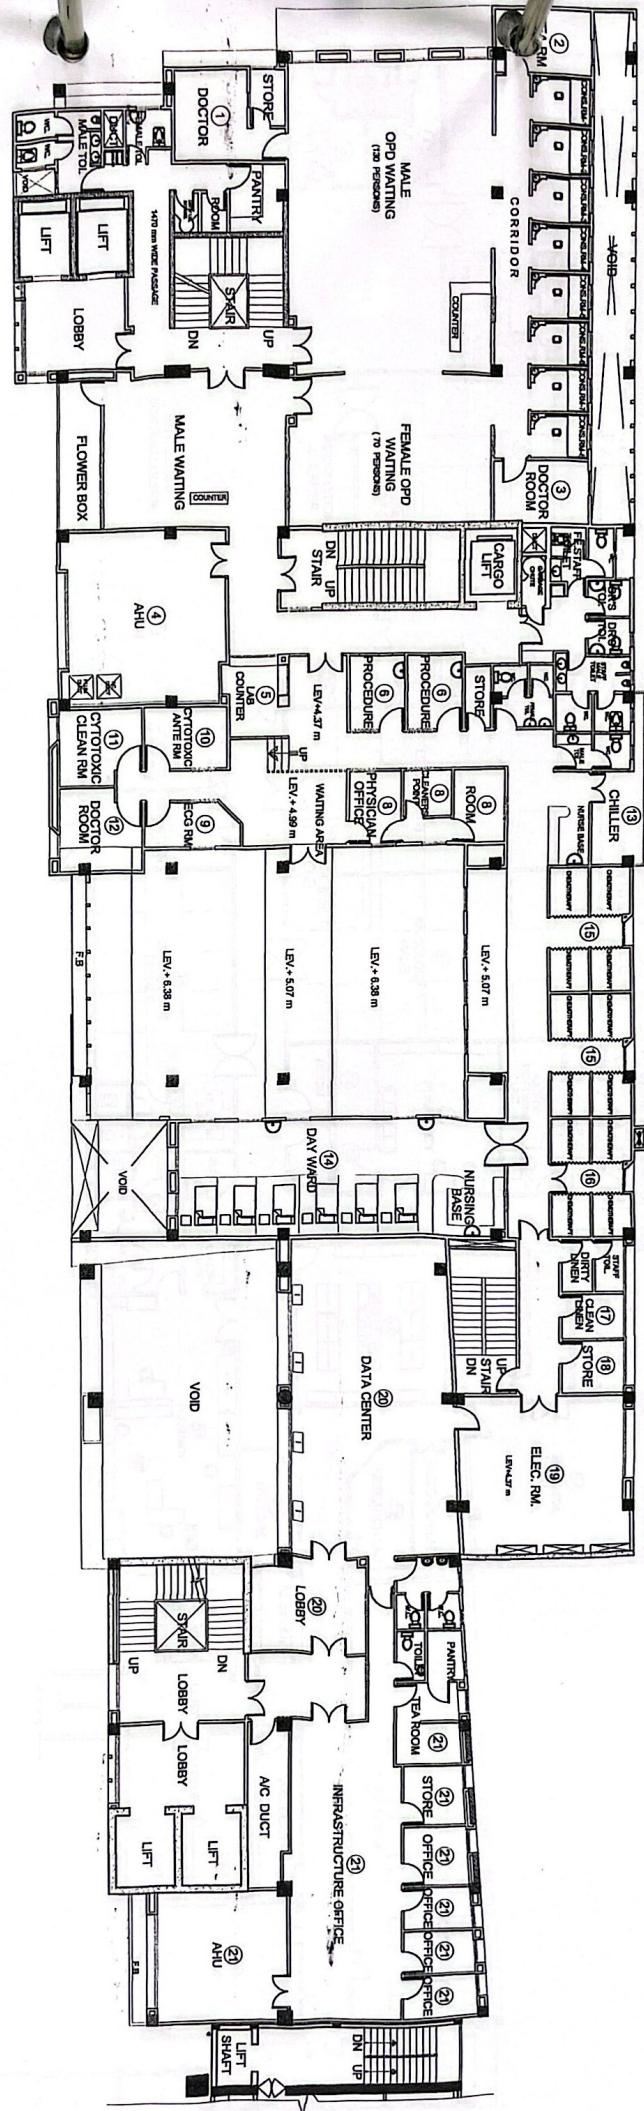


2ND. FLOOR PLAN

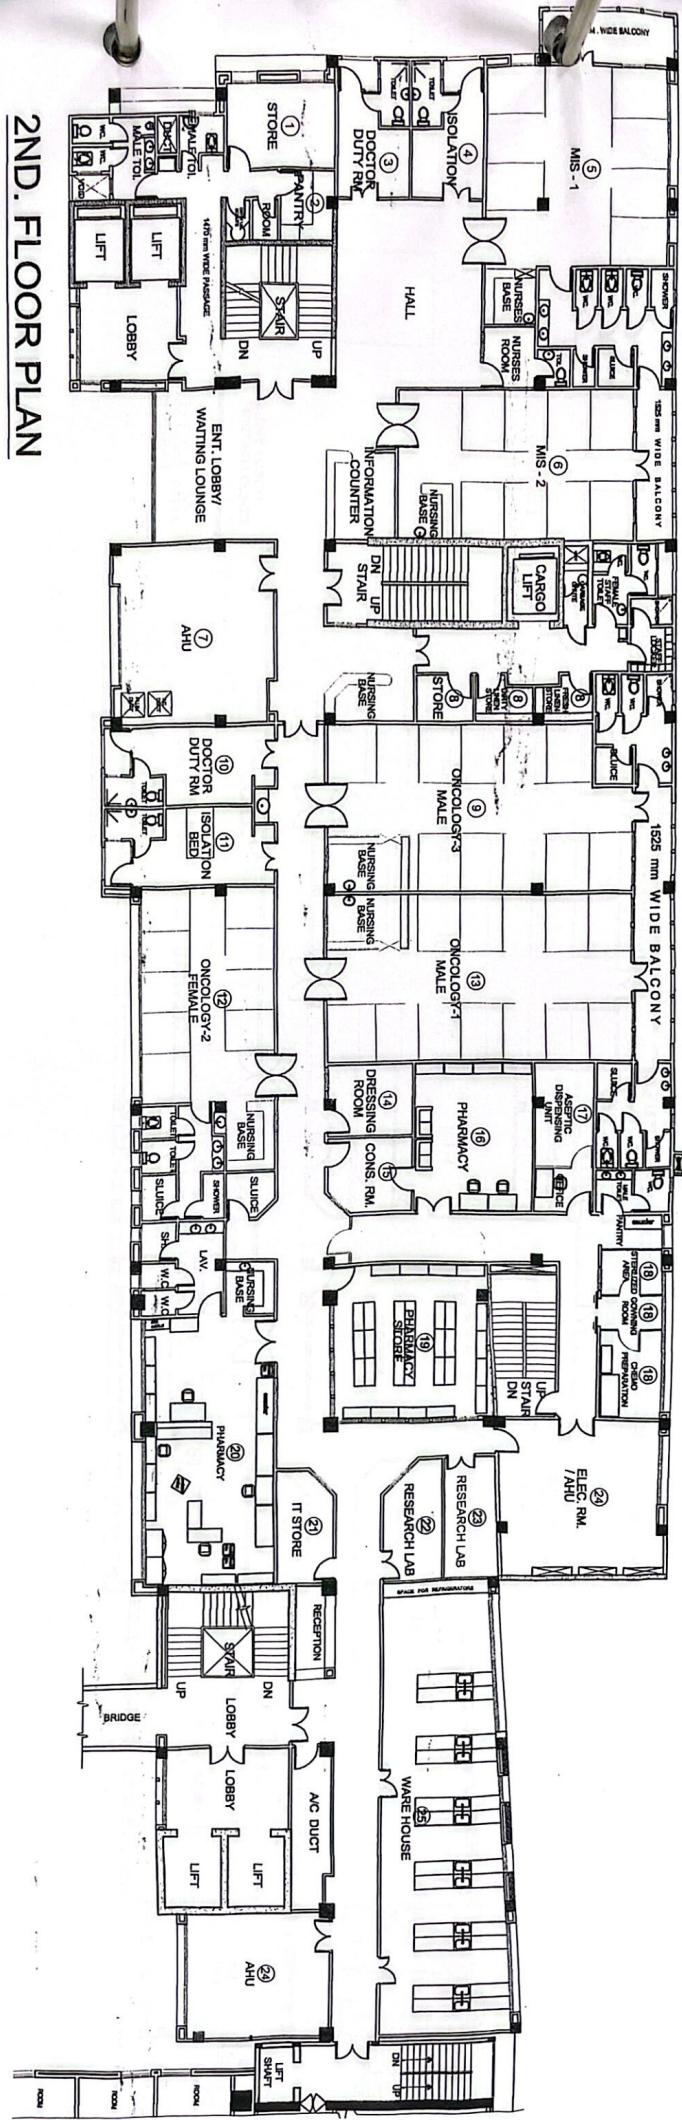


3RD. FLOOR PLAN

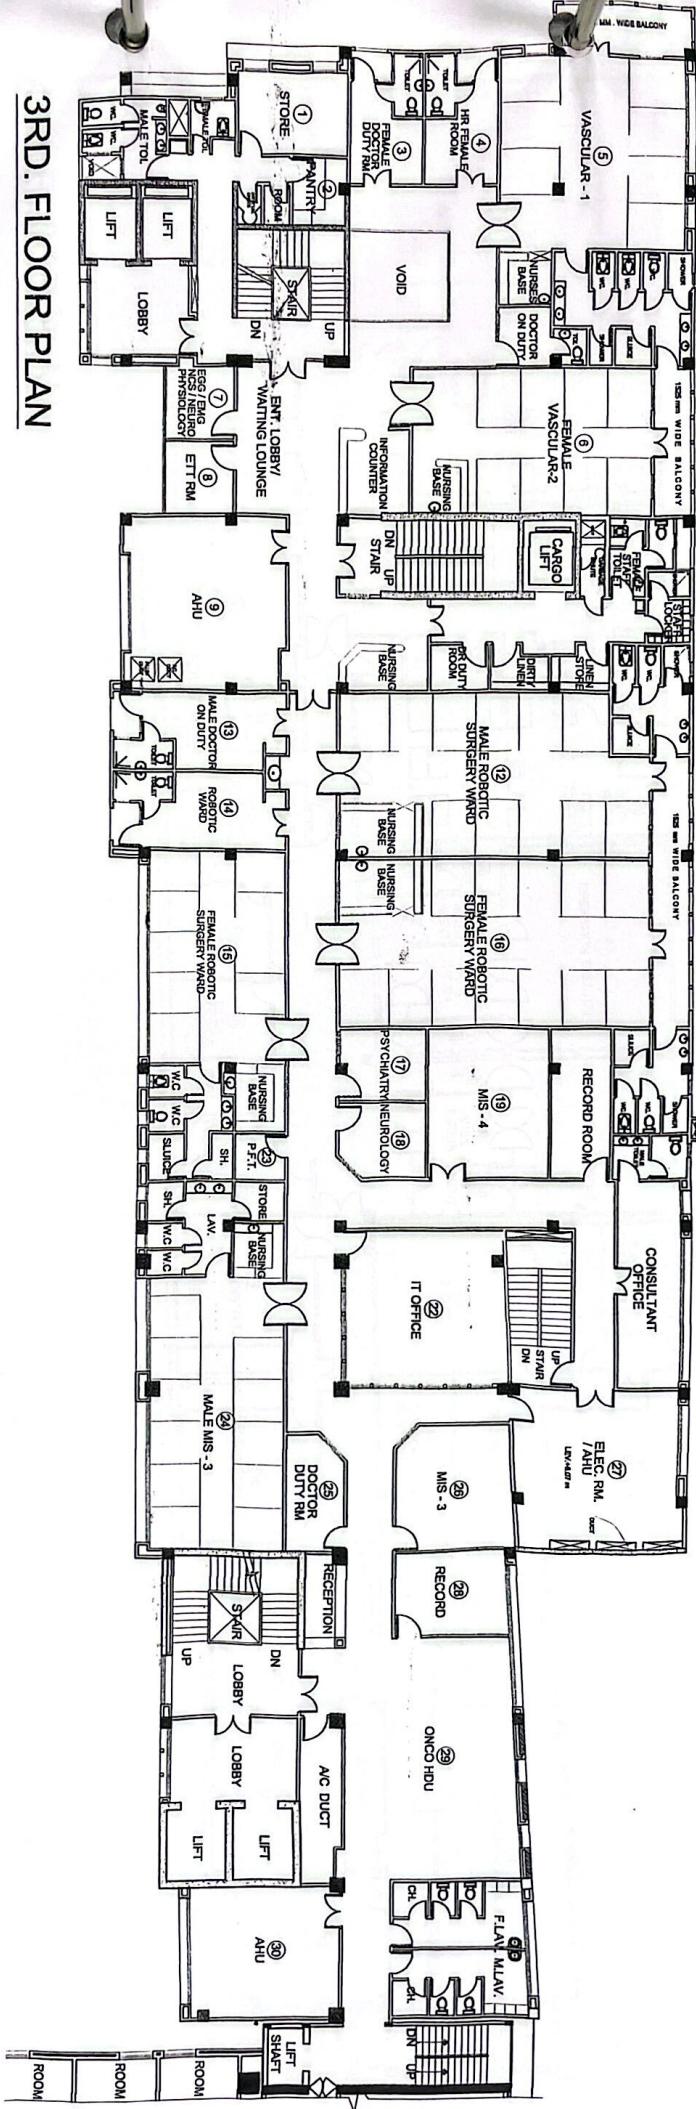

4TH. FLOOR PLAN

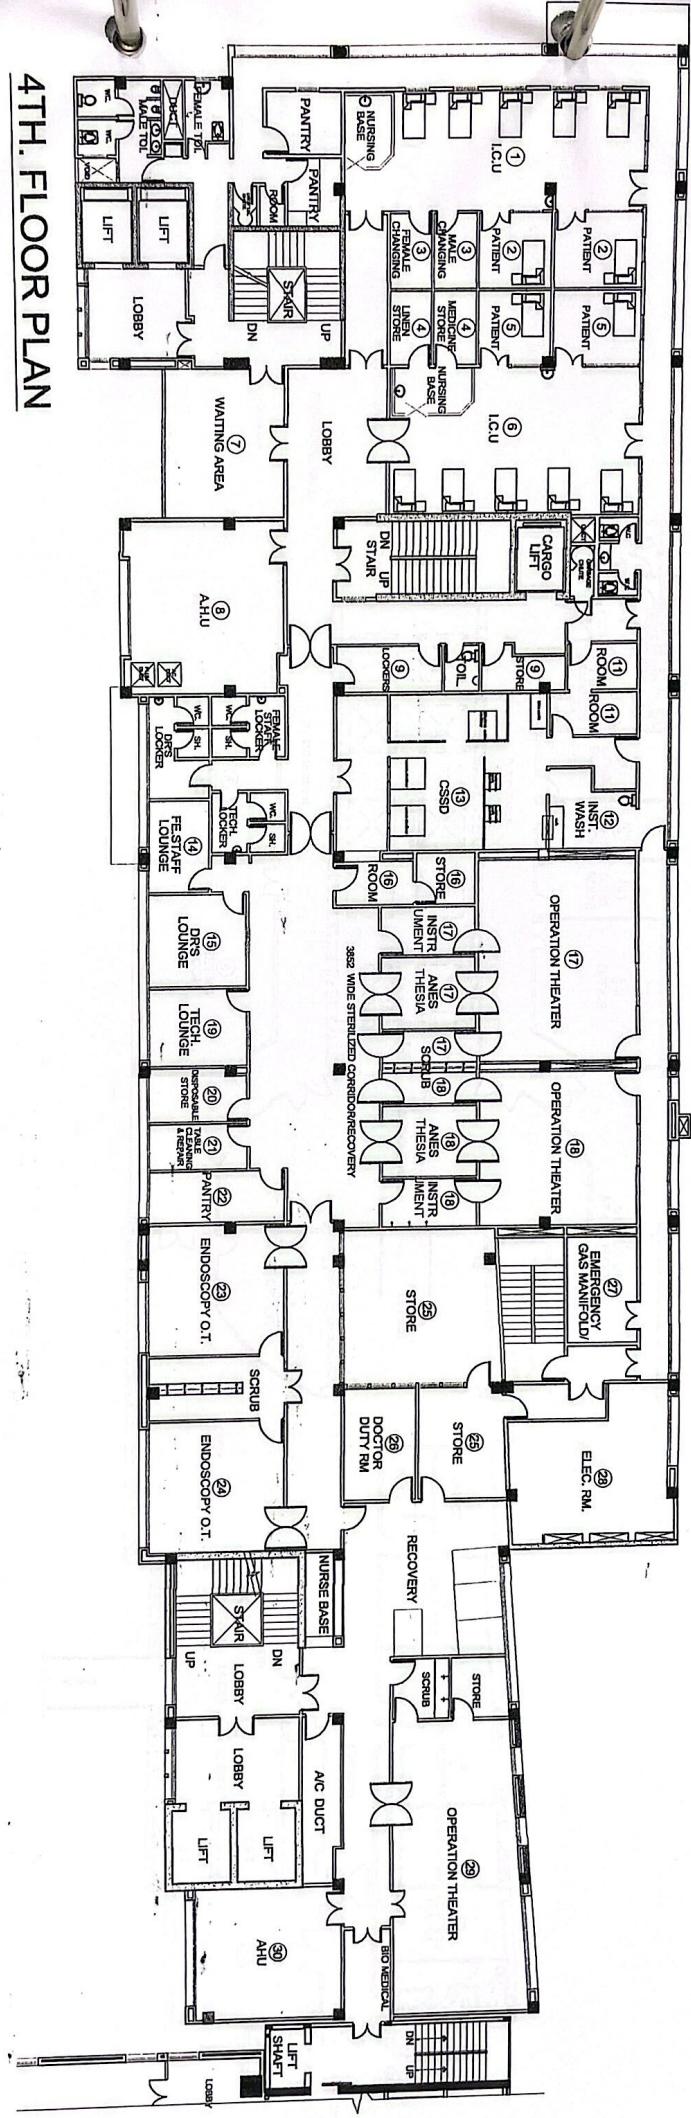

5TH. FLOOR PLAN

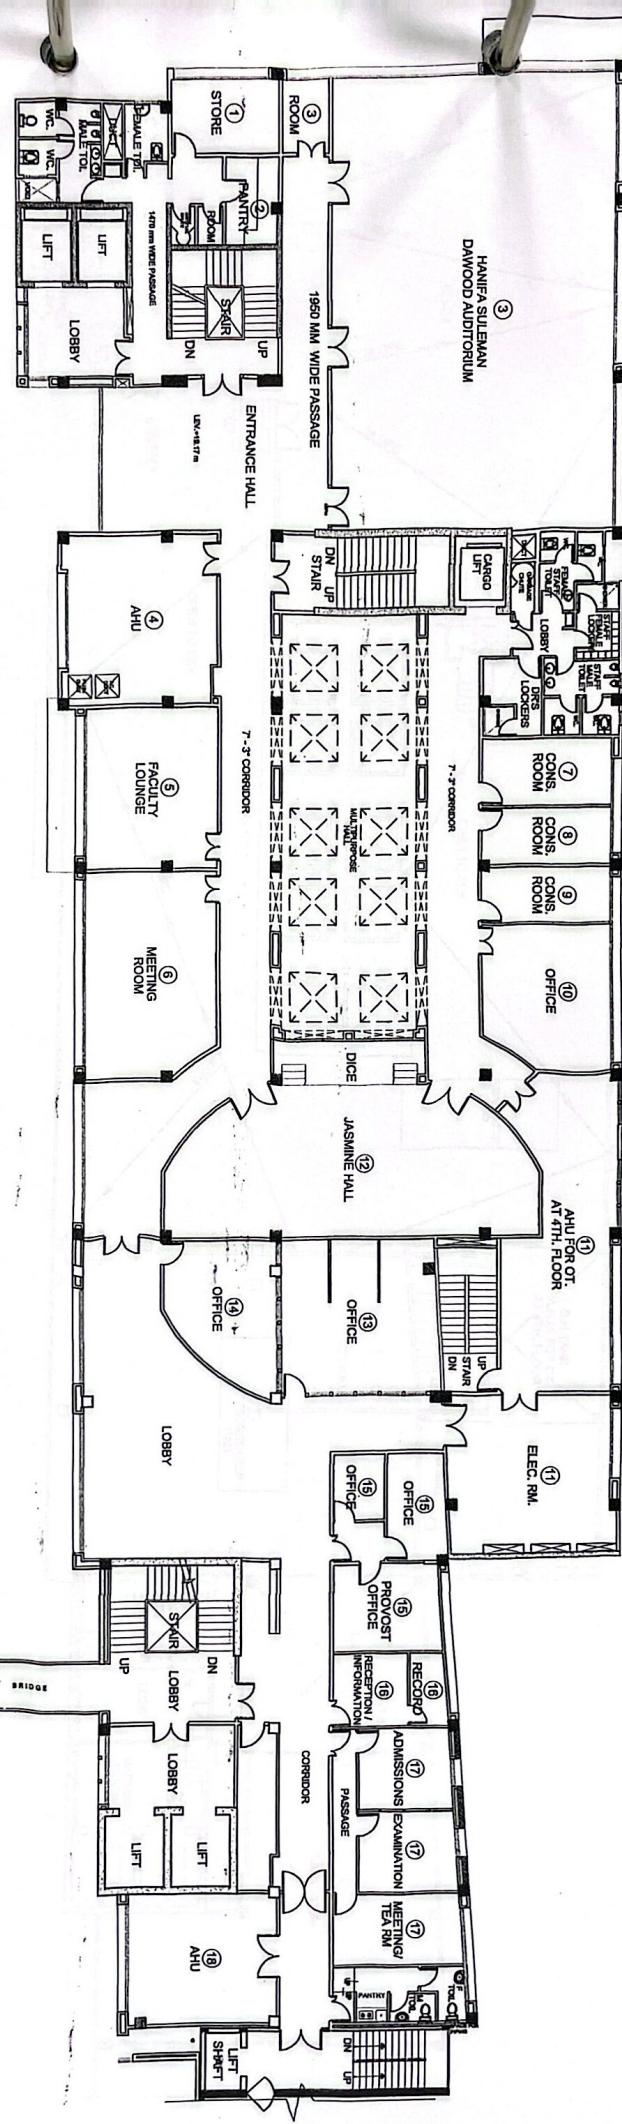

ROOF PLAN

